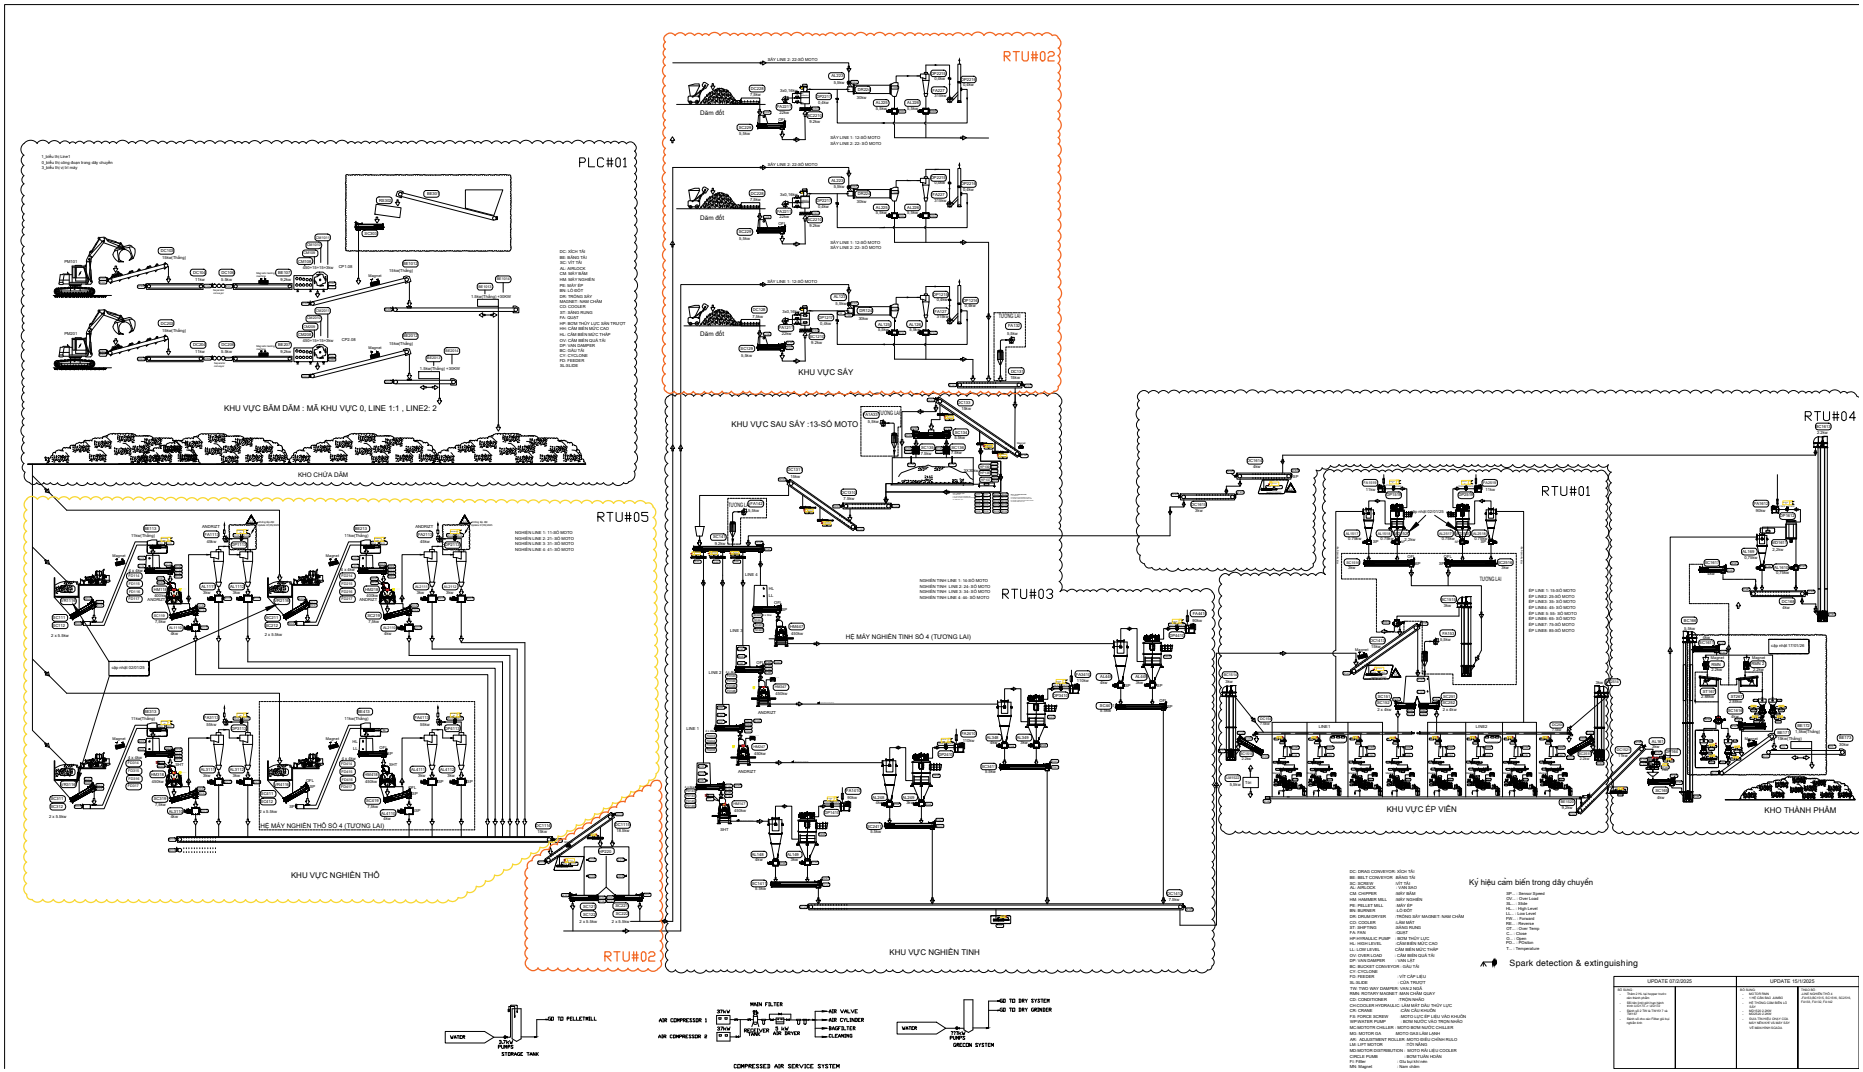

PLC#01
KHU VỰC BĂM DĂM : MÃ KHU VỰC 0, LINE 1:1 , LINE2: 2
KHO CHỨA DĂM
RTU#02
KHU VỰC SẤY
KHU VỰC SAU SẤY :13-SỐ MOTO
RTU#03
KHU VỰC NGHIỀN TINH
RTU#05
KHU VỰC NGHIỀN THÔ
RTU#01
RTU#04
KHU VỰC ÉP VIÊN
KHO THÀNH PHẨM
GO TO PELLETMILL
STORAGE TANK
COMPRESSED AIR SERVICE SYSTEM
GO TO DRY SYSTEM
GO TO DRY GRINDER
GREEN SYSTEM
Ký hiệu cảm biến trong dây chuyền
Spark detection & extinguishing